

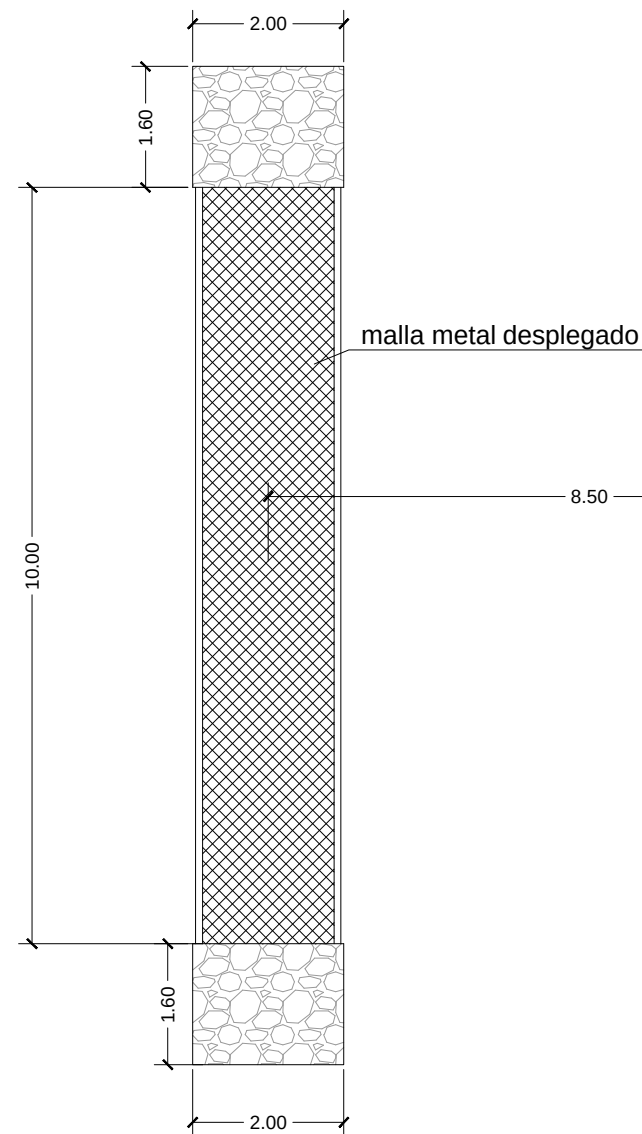


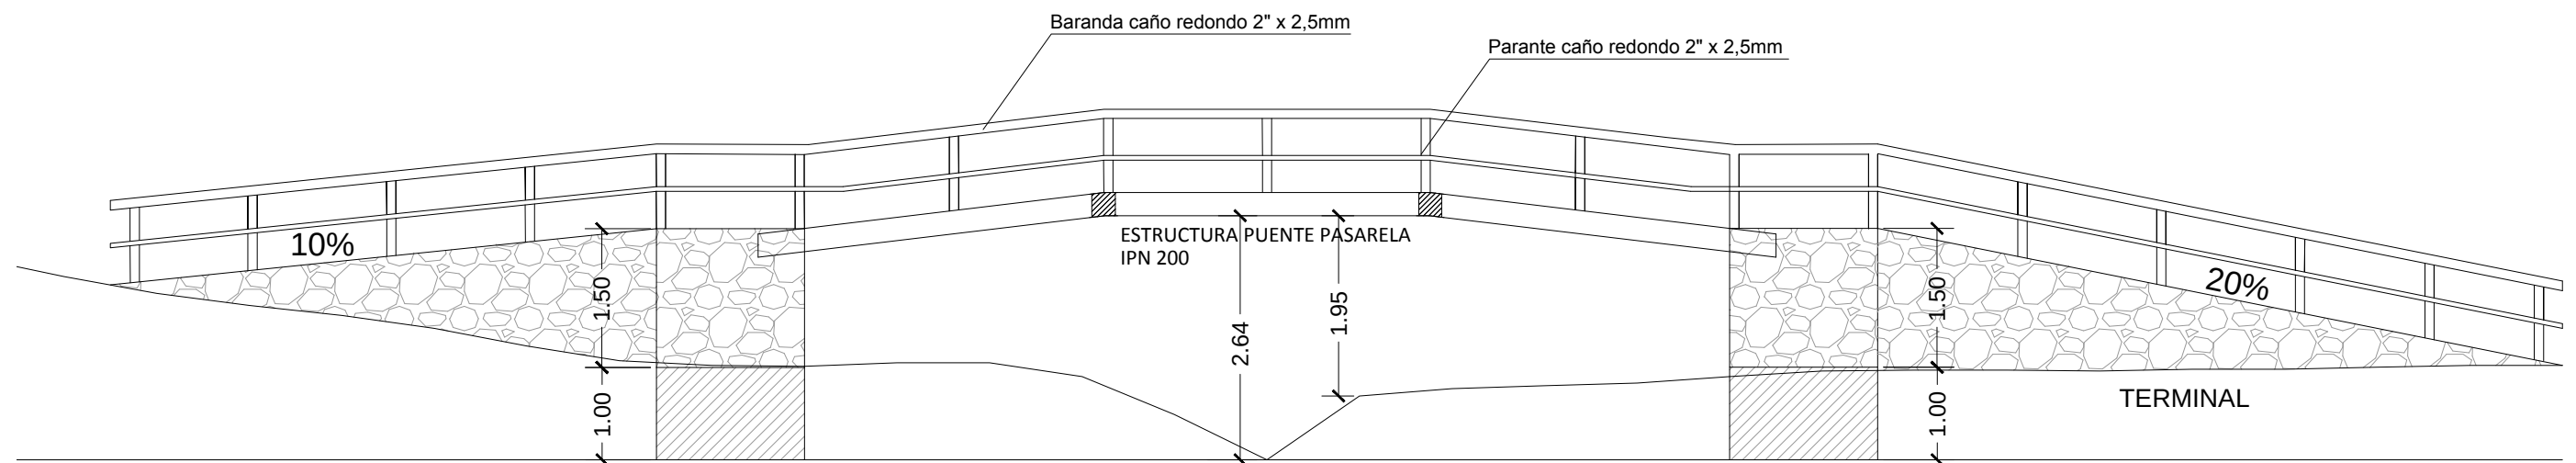

VADO EXISTENTE

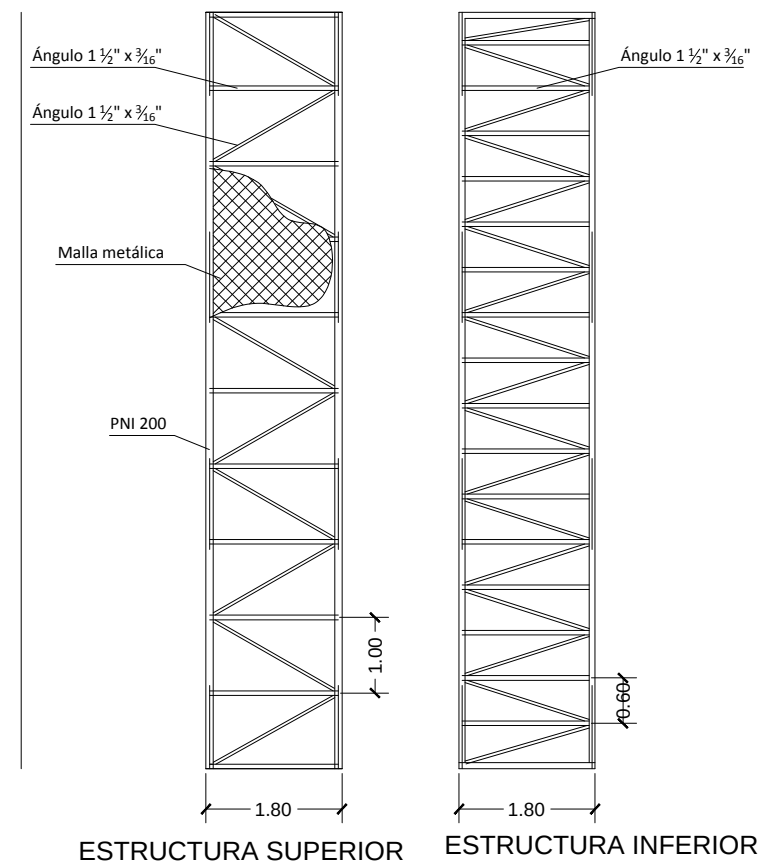

MUNICIPALIDAD DE ALTA GRACIA

SECRETARIA DE INFRAESTRUCTURA

OBRA: PROYECTO CICLOVÍA EN LA COSTANERA DE ARROYO CHICAMTOLTINA

PIEZA GRÁFICA: PLANTA Y CORTE DE PASALERA SOBRE ARROYO CHICAMTOLTINA Escala: 1:75/1:100

Arq. Marcos A. Moreira - Director de Obras Públicas